
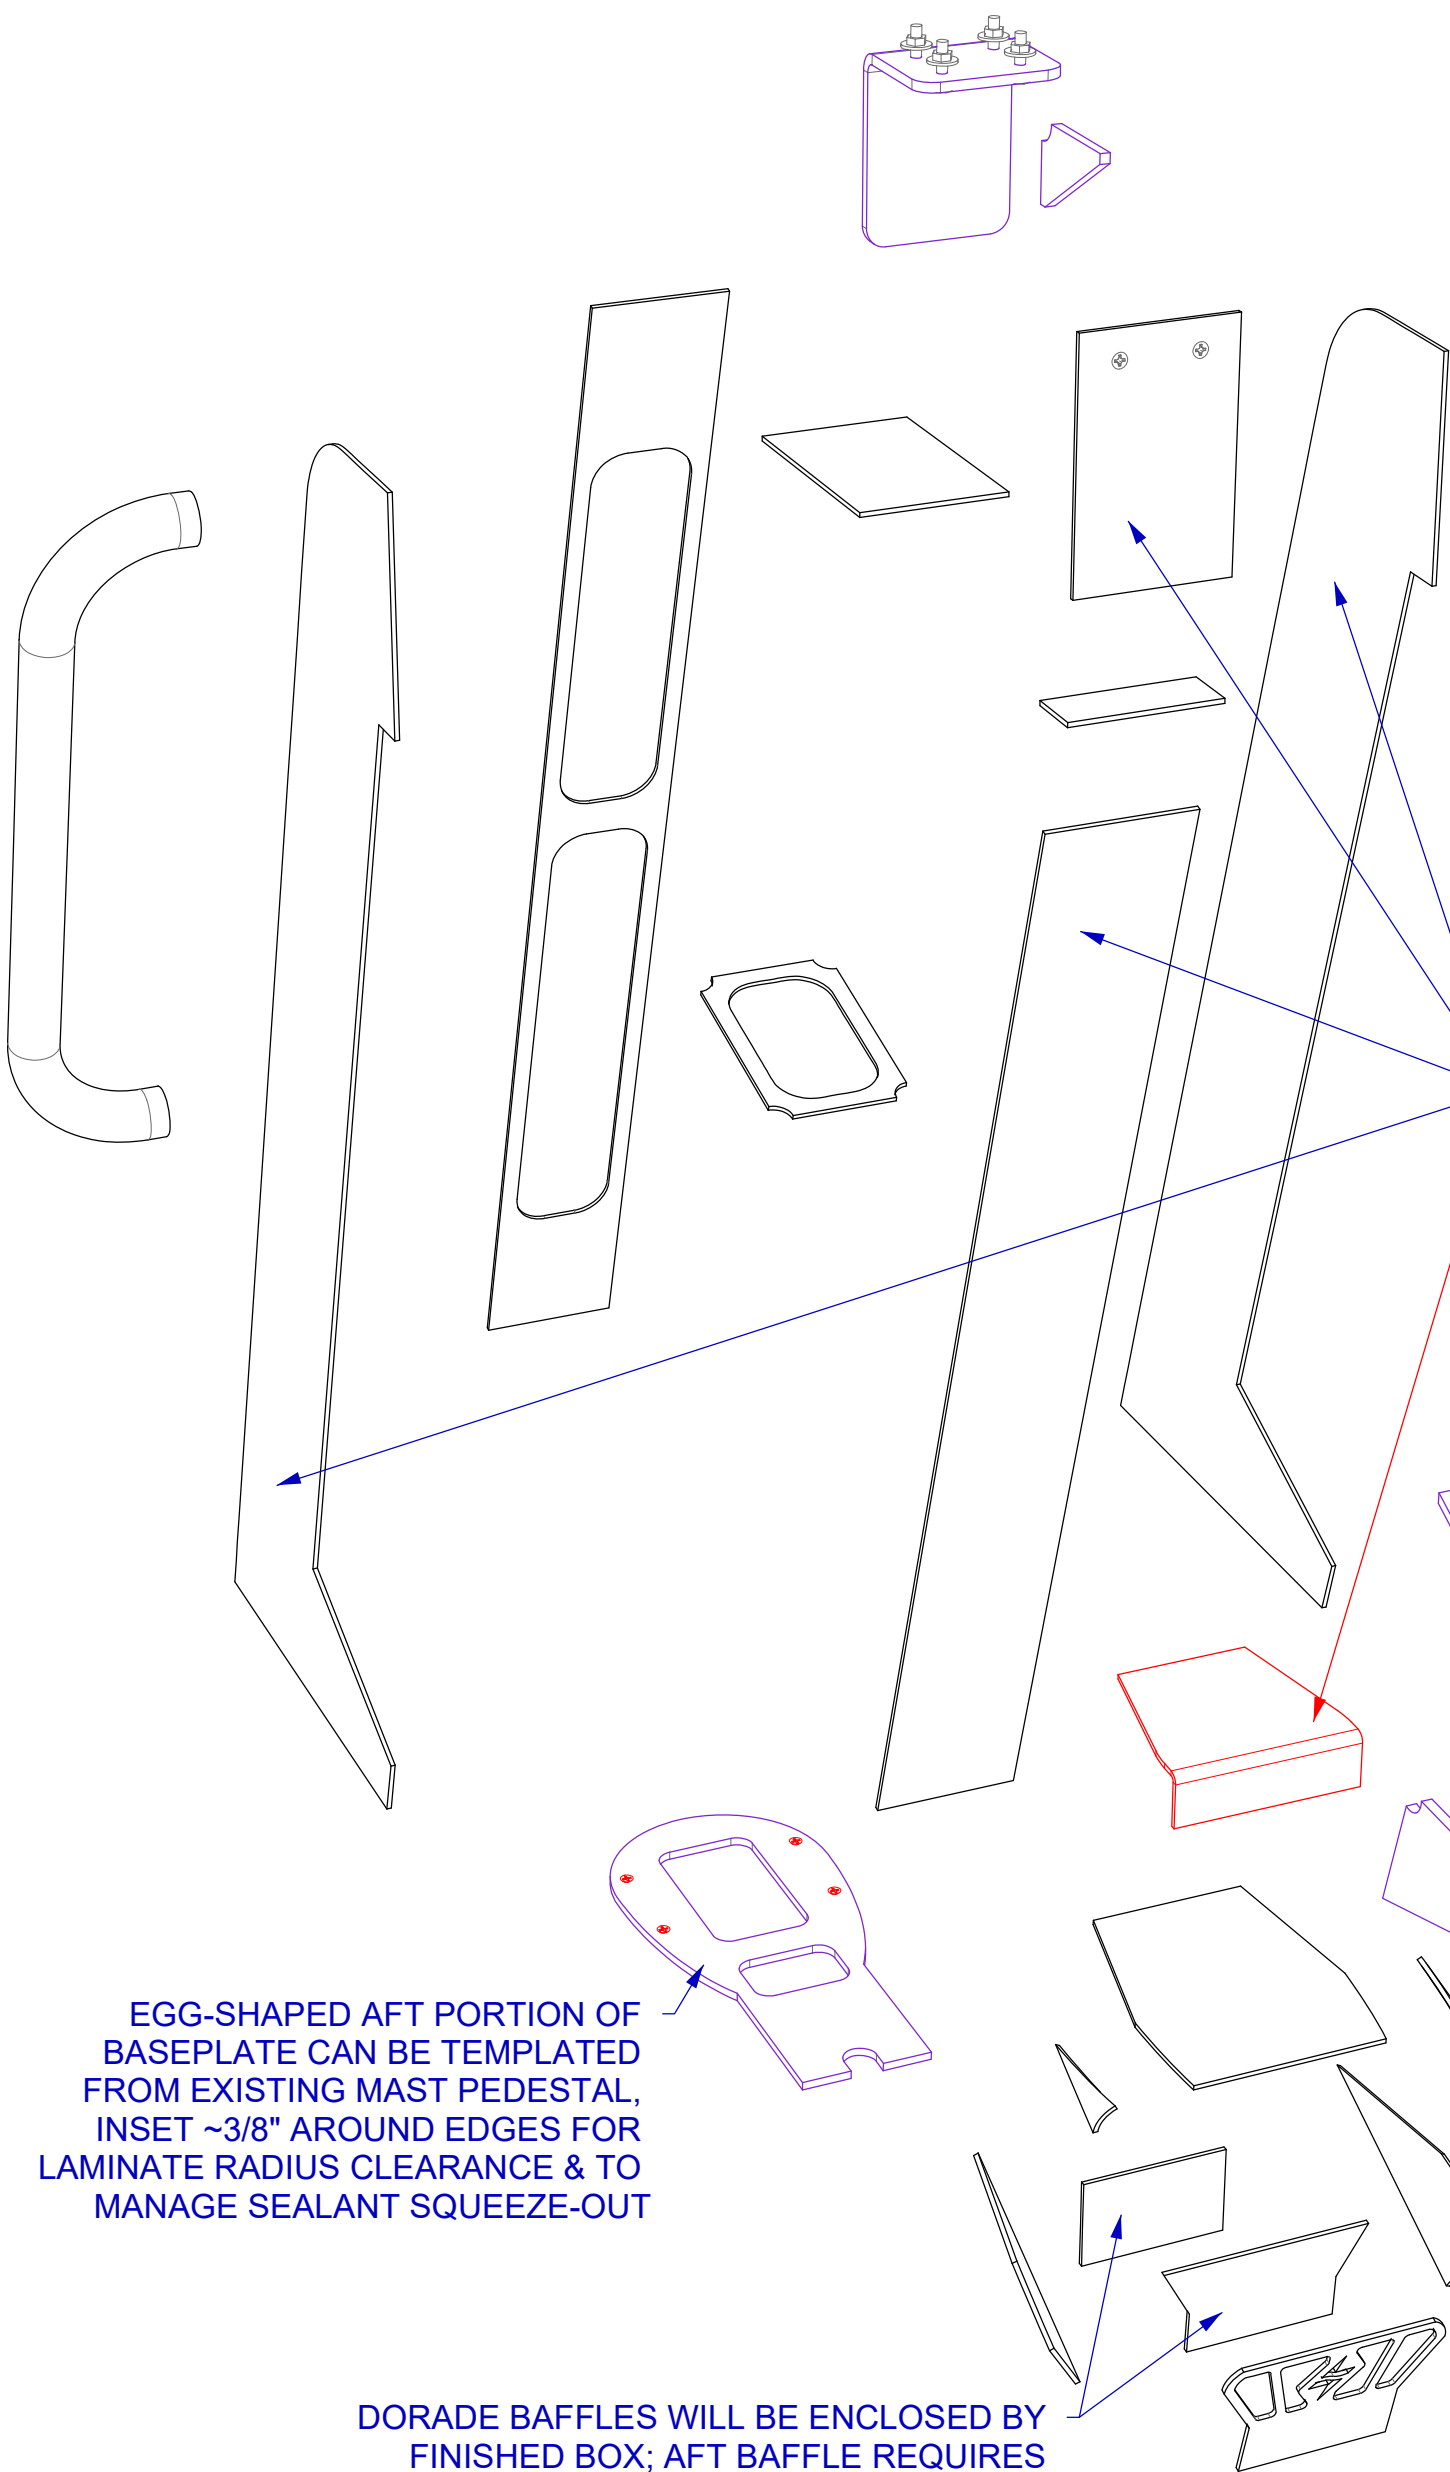


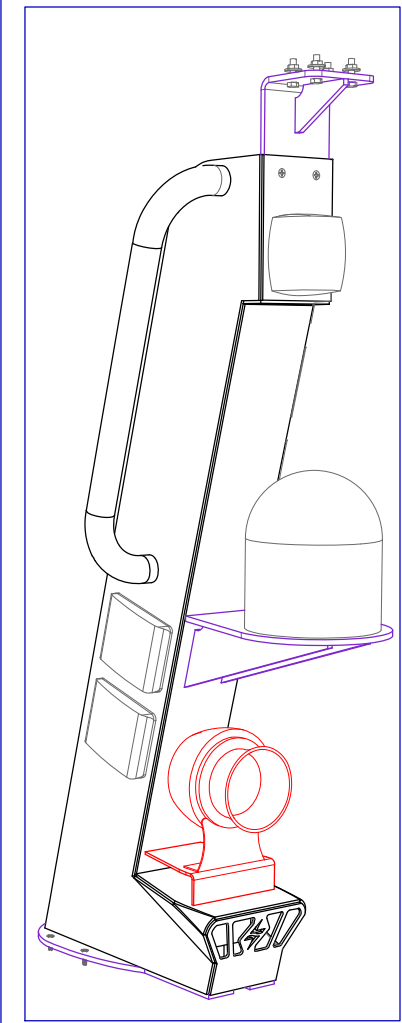

WIREWAY /
INSTALLATION
CUT-OUTS FOR
INSTRUMENTS &
INLETS NOT SHOWN;
MARK FROM PARTS
& CUT AS NEEDED

EGG-SHAPED AFT PORTION OF
BASEPLATE CAN BE TEMPLATED
FROM EXISTING MAST PEDESTAL,
INSET ~3/8" AROUND EDGES FOR
LAMINATE RADIUS CLEARANCE & TO
MANAGE SEALANT SQUEEZE-OUT

DORADE BAFFLES WILL BE ENCLOSED BY
FINISHED BOX; AFT BAFFLE REQUIRES
WATERTIGHT JOINT ON BOTTOM (AGAINST
BASEPLATE) & SIDES. WELD SEQUENCE TBD,
FLANGES & PLUG WELDS MAY BE REQUIRED

PRELIMINARY
NOT FOR
CONSTRUCTION

SOLANDER 38
FORWARD MAST
ALUM. PARTS EXPLODED
3"=1'-0" / 11" X 17"
HJN 4 MAY 2026
SHEET 4 OF 5

PURPLE: 1/4" ALUM. 5052

ALL OTHER FLAT PLATE PARTS 1/8" ALUM. 6061