


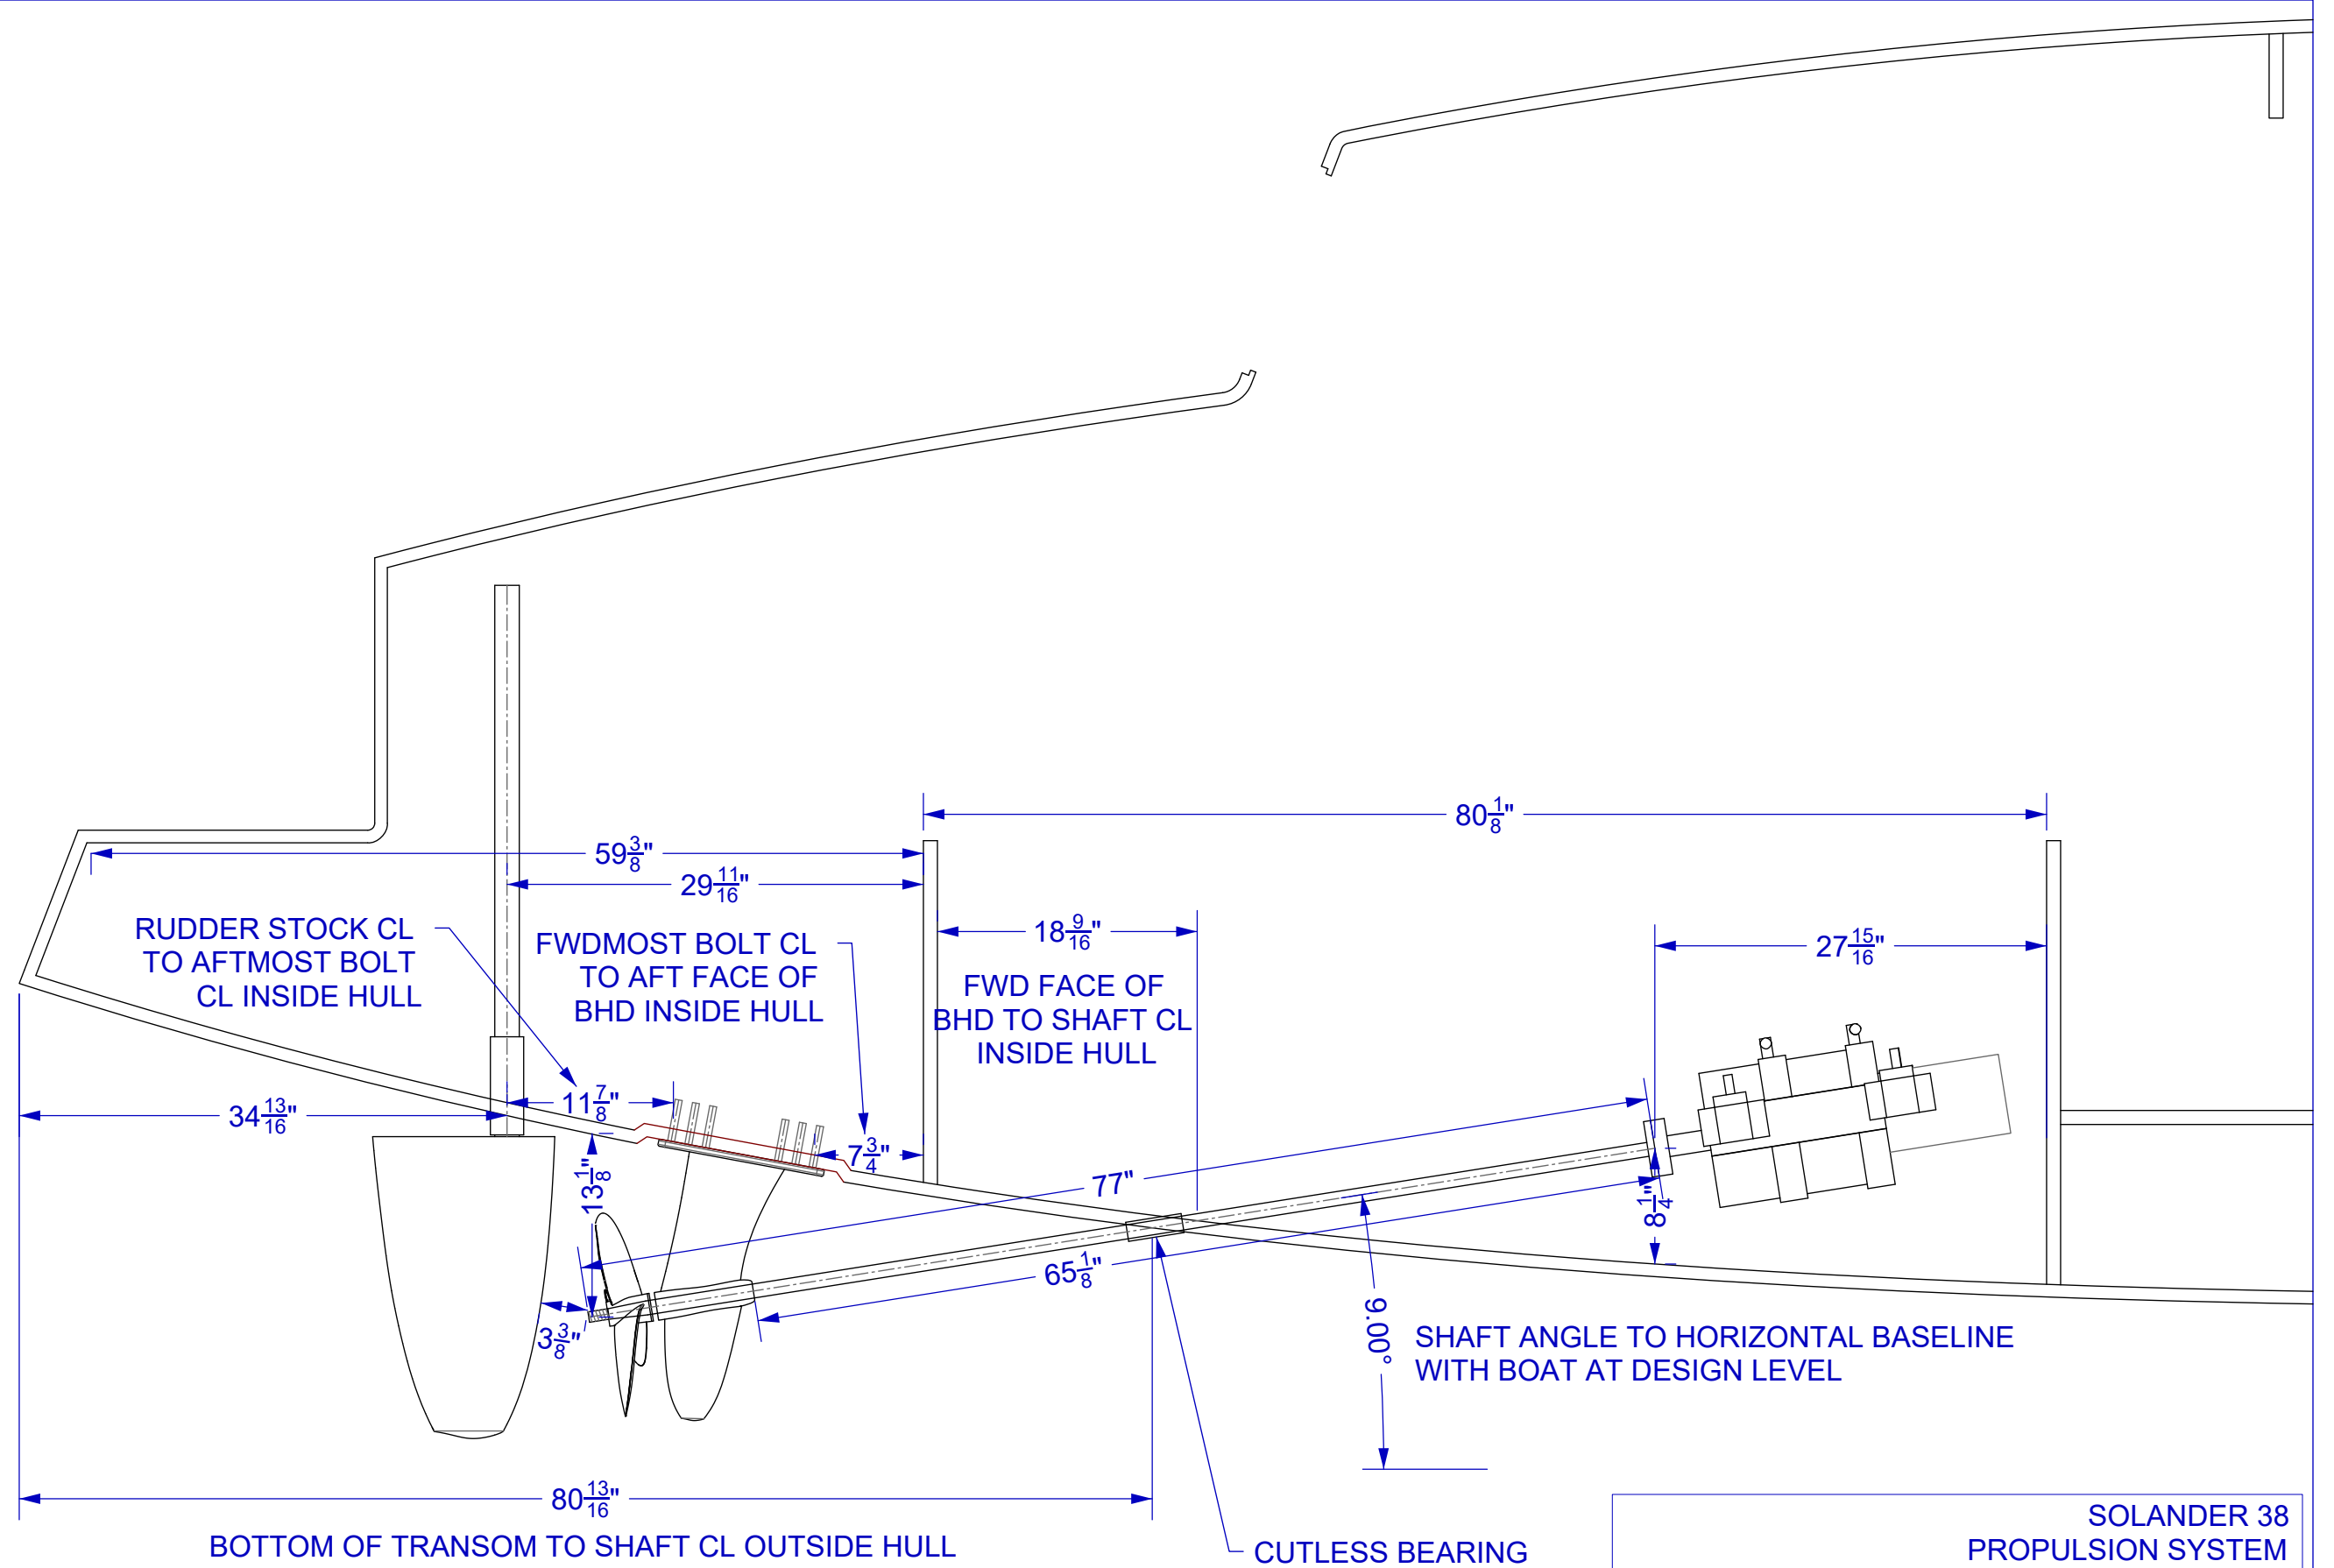

SOLANDER 38
 PROPULSION SYSTEM
 PROFILE SECTION AT STBD HULL CENTERLINE
 1"=1'-0"
 HJN 9/12/24