



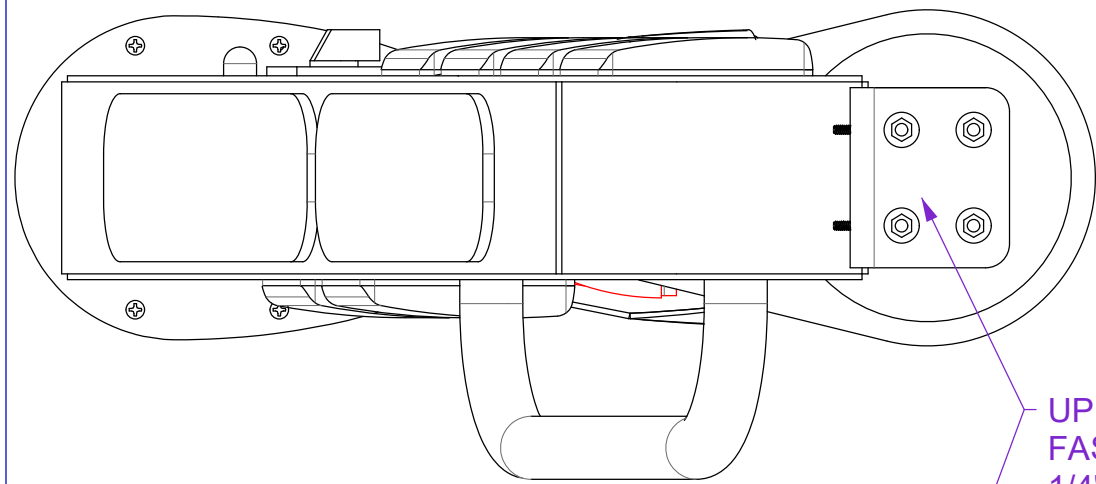


UPPER FLANGE 1/4" ALUM. 5052
FASTENS TO EXIST. SUPERSTRUCTURE CANOPY W/
1/4" HEX BOLTS & NUTS (X4); FASTENS TO MAST W/
10-24 316L STN STL FLATHEAD SCREWS (X2) - TAP &
COUNTERSINK

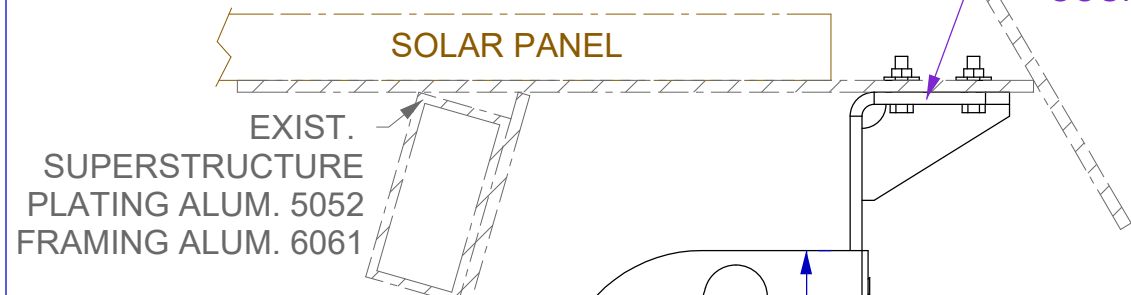

SOLAR PANEL

EXIST.
SUPERSTRUCTURE
PLATING ALUM. 5052
FRAMING ALUM. 6061

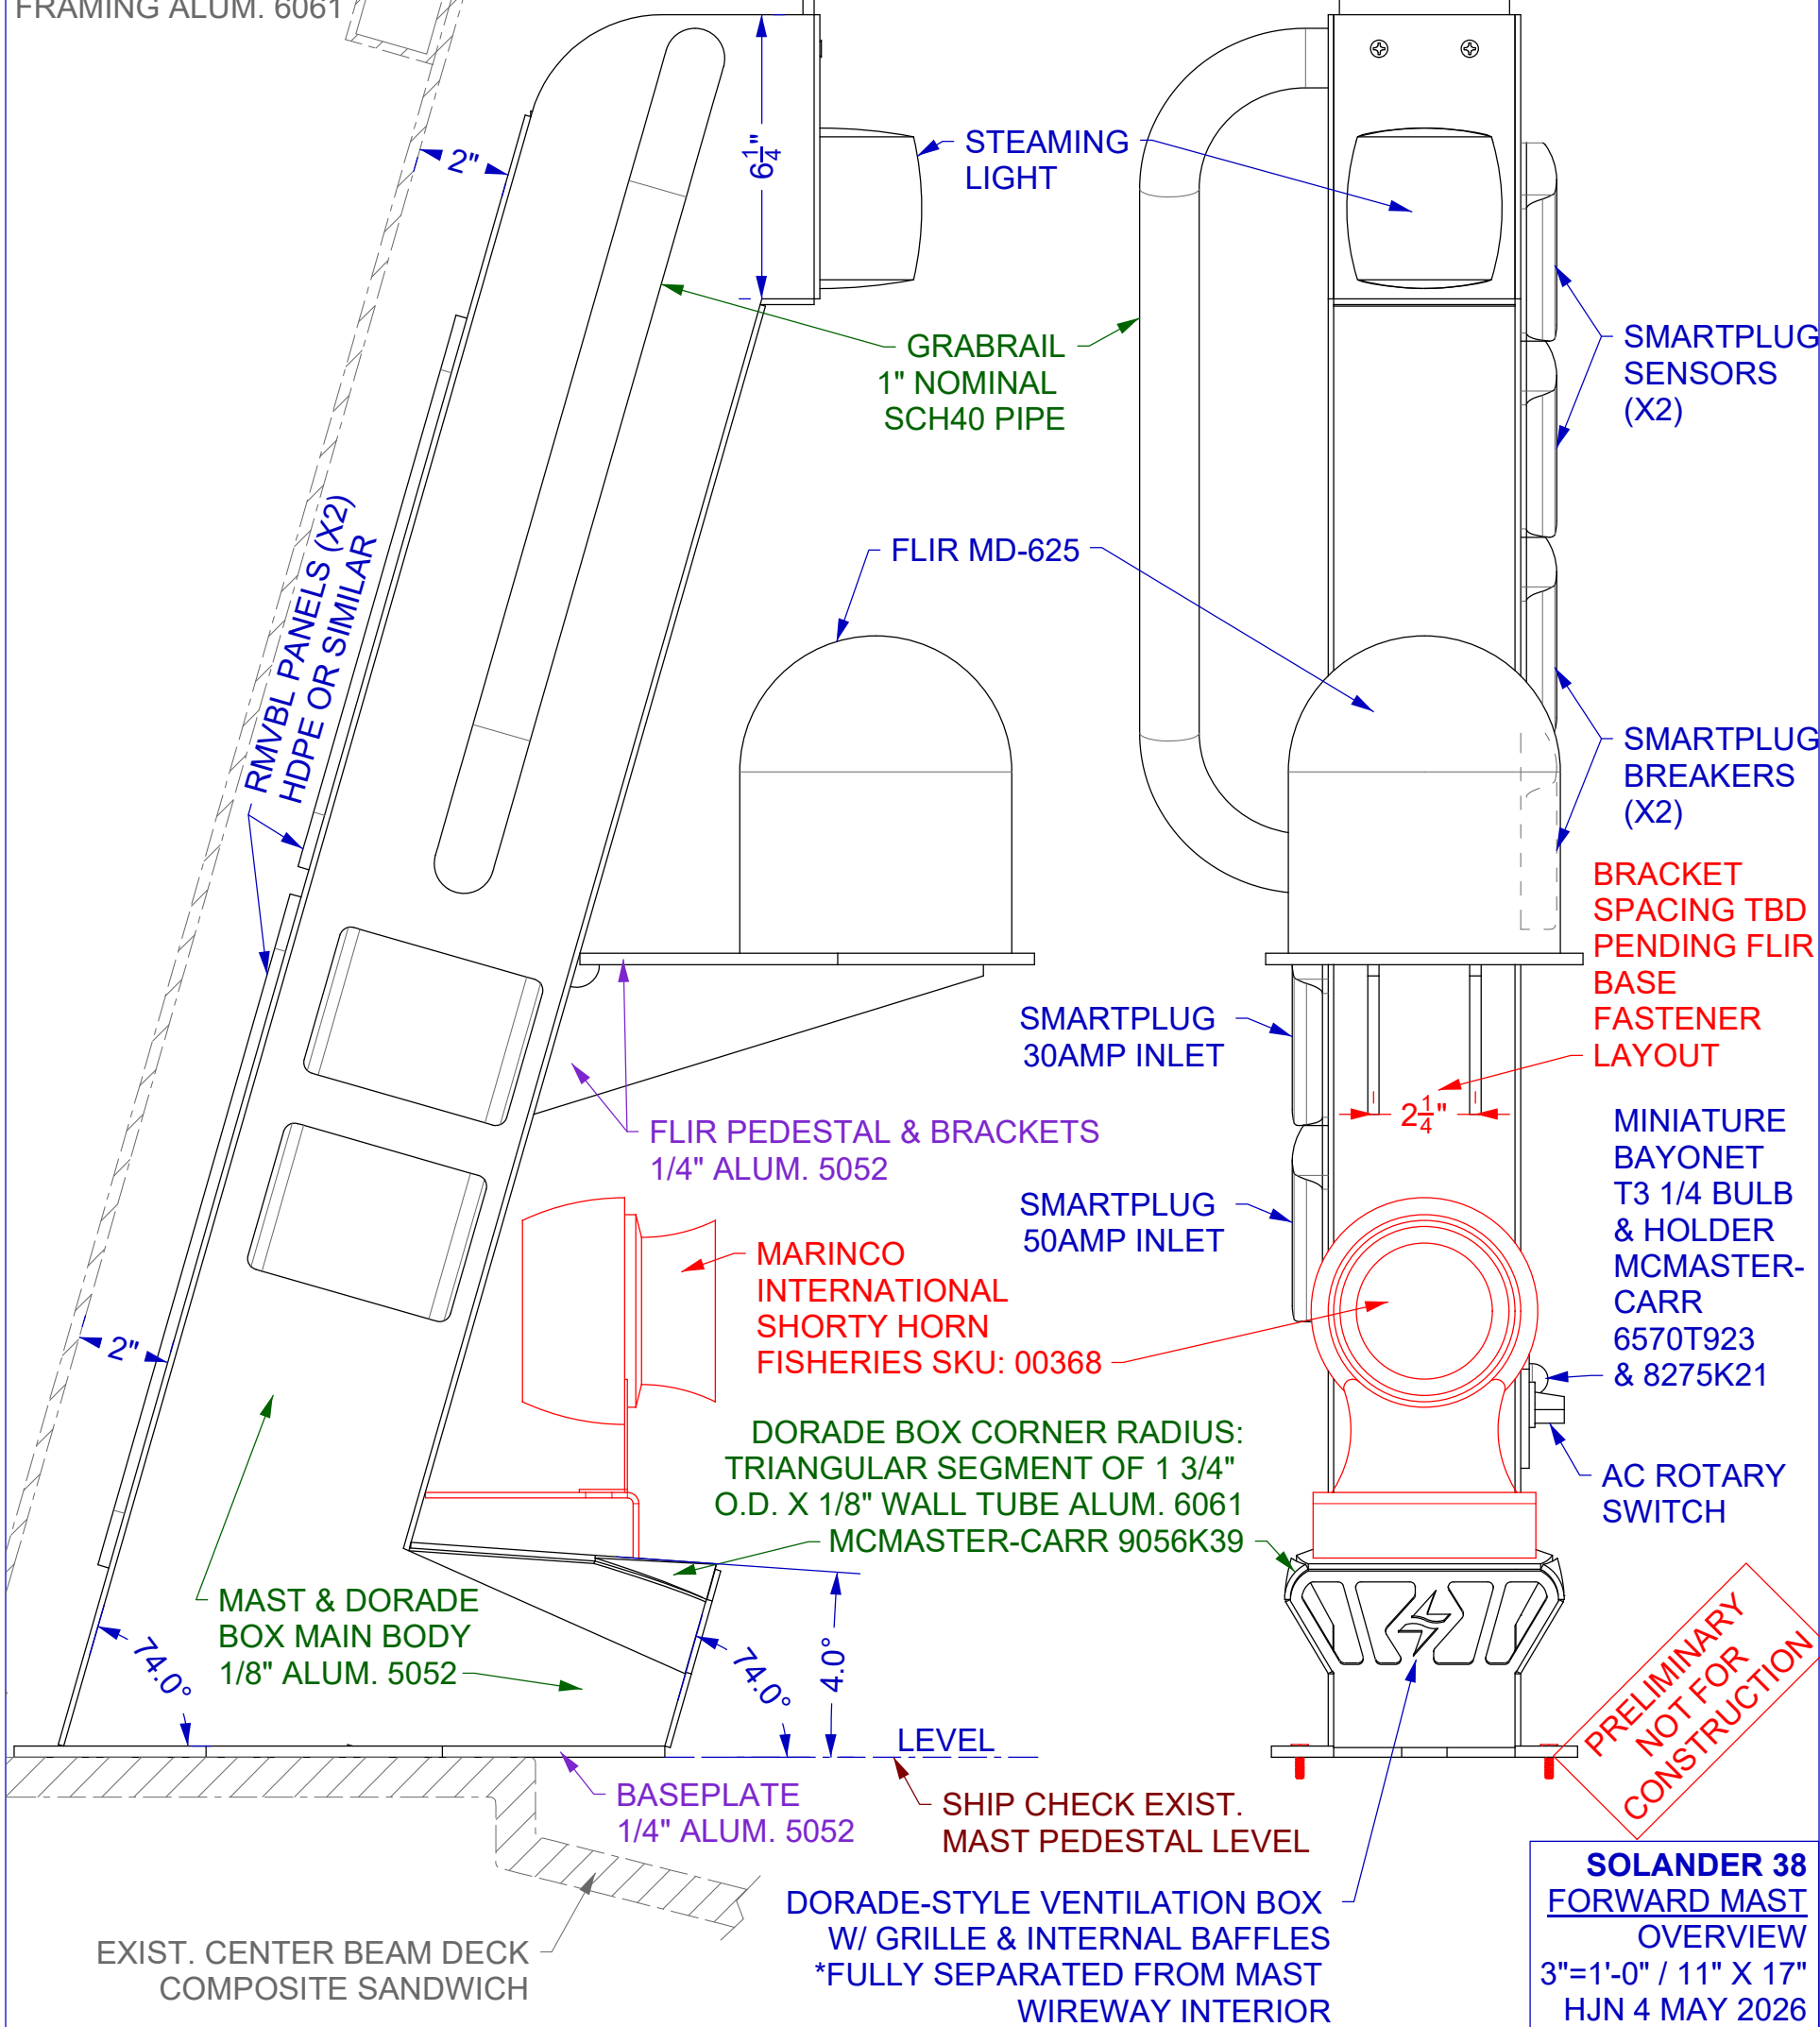

SOLANDER 38
FORWARD MAST
OVERVIEW
3"=1'-0" / 11" X 17"
HJN 4 MAY 2026
SHEET 2 OF 5