


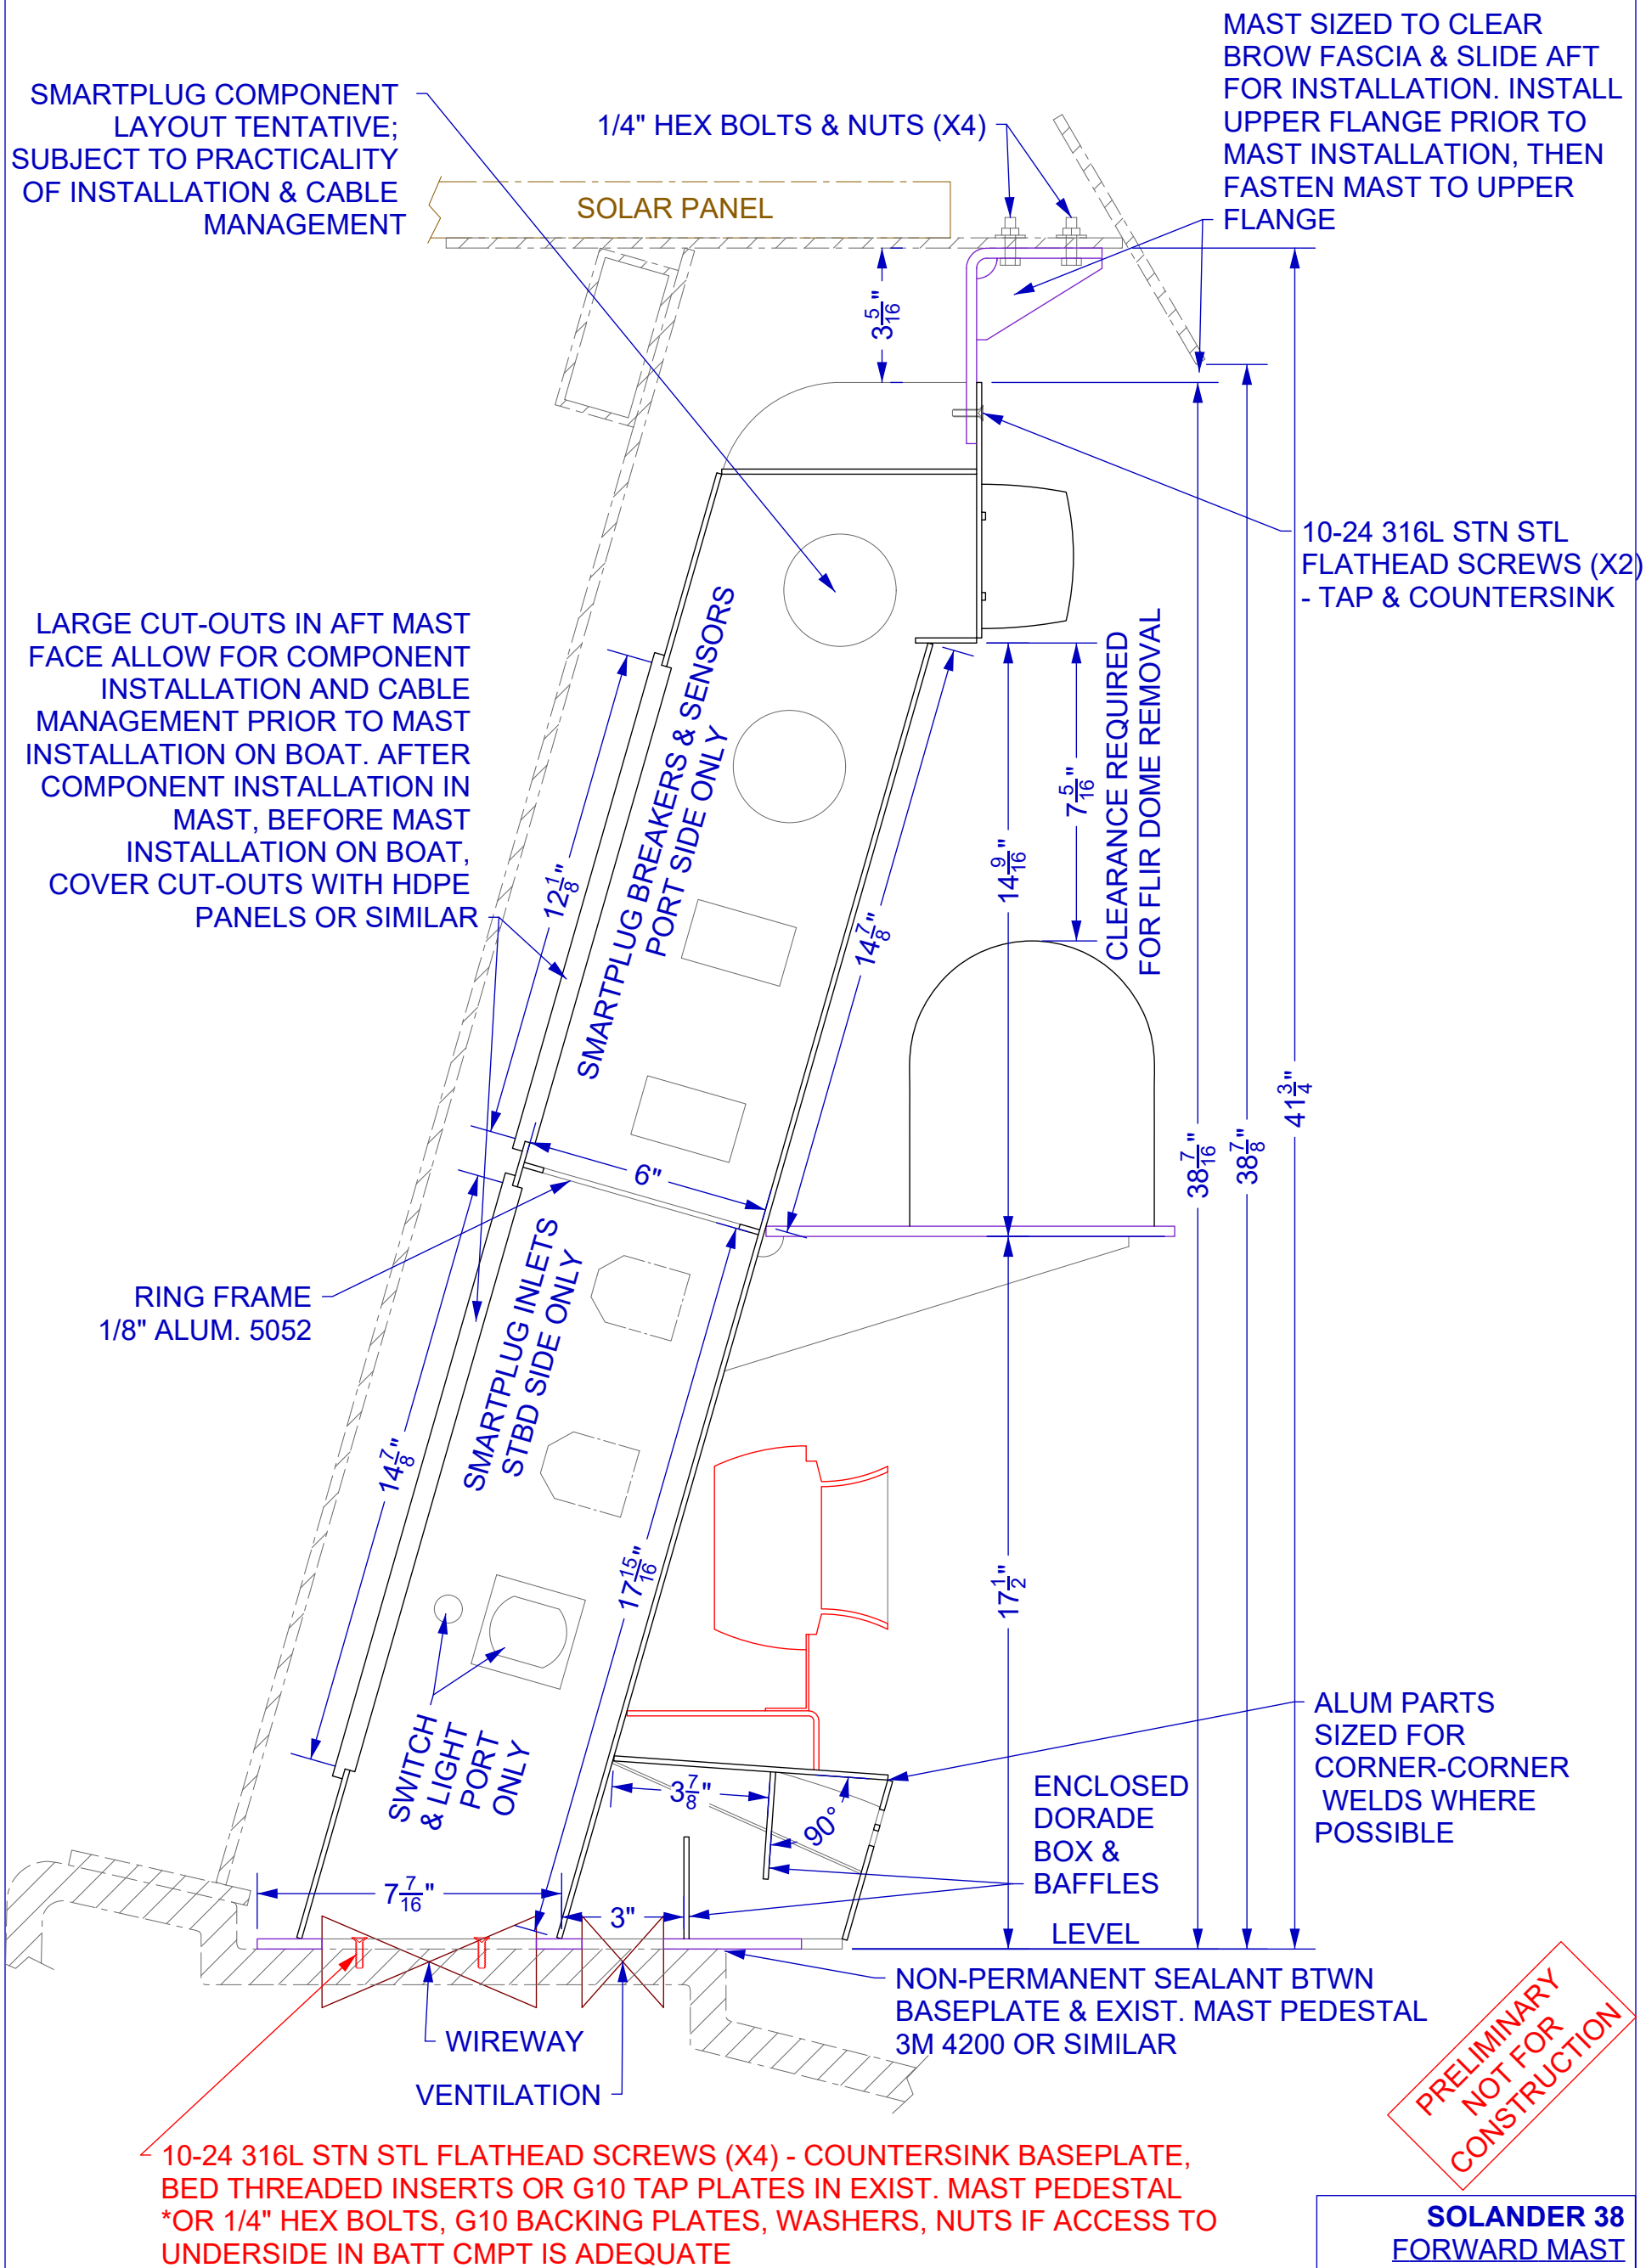

PRELIMINARY
NOT FOR
CONSTRUCTION

SOLANDER 38
FORWARD MAST
INBOARD PROFILE
(LONG'L SECT. AT CL)
3"=1'-0" / 11" X 17"
HJN 4 MAY 2026
SHEET 3 OF 5

PURPLE: 1/4" ALUM. 5052

ALL OTHER FLAT PLATE PARTS 1/8" ALUM. 6061