


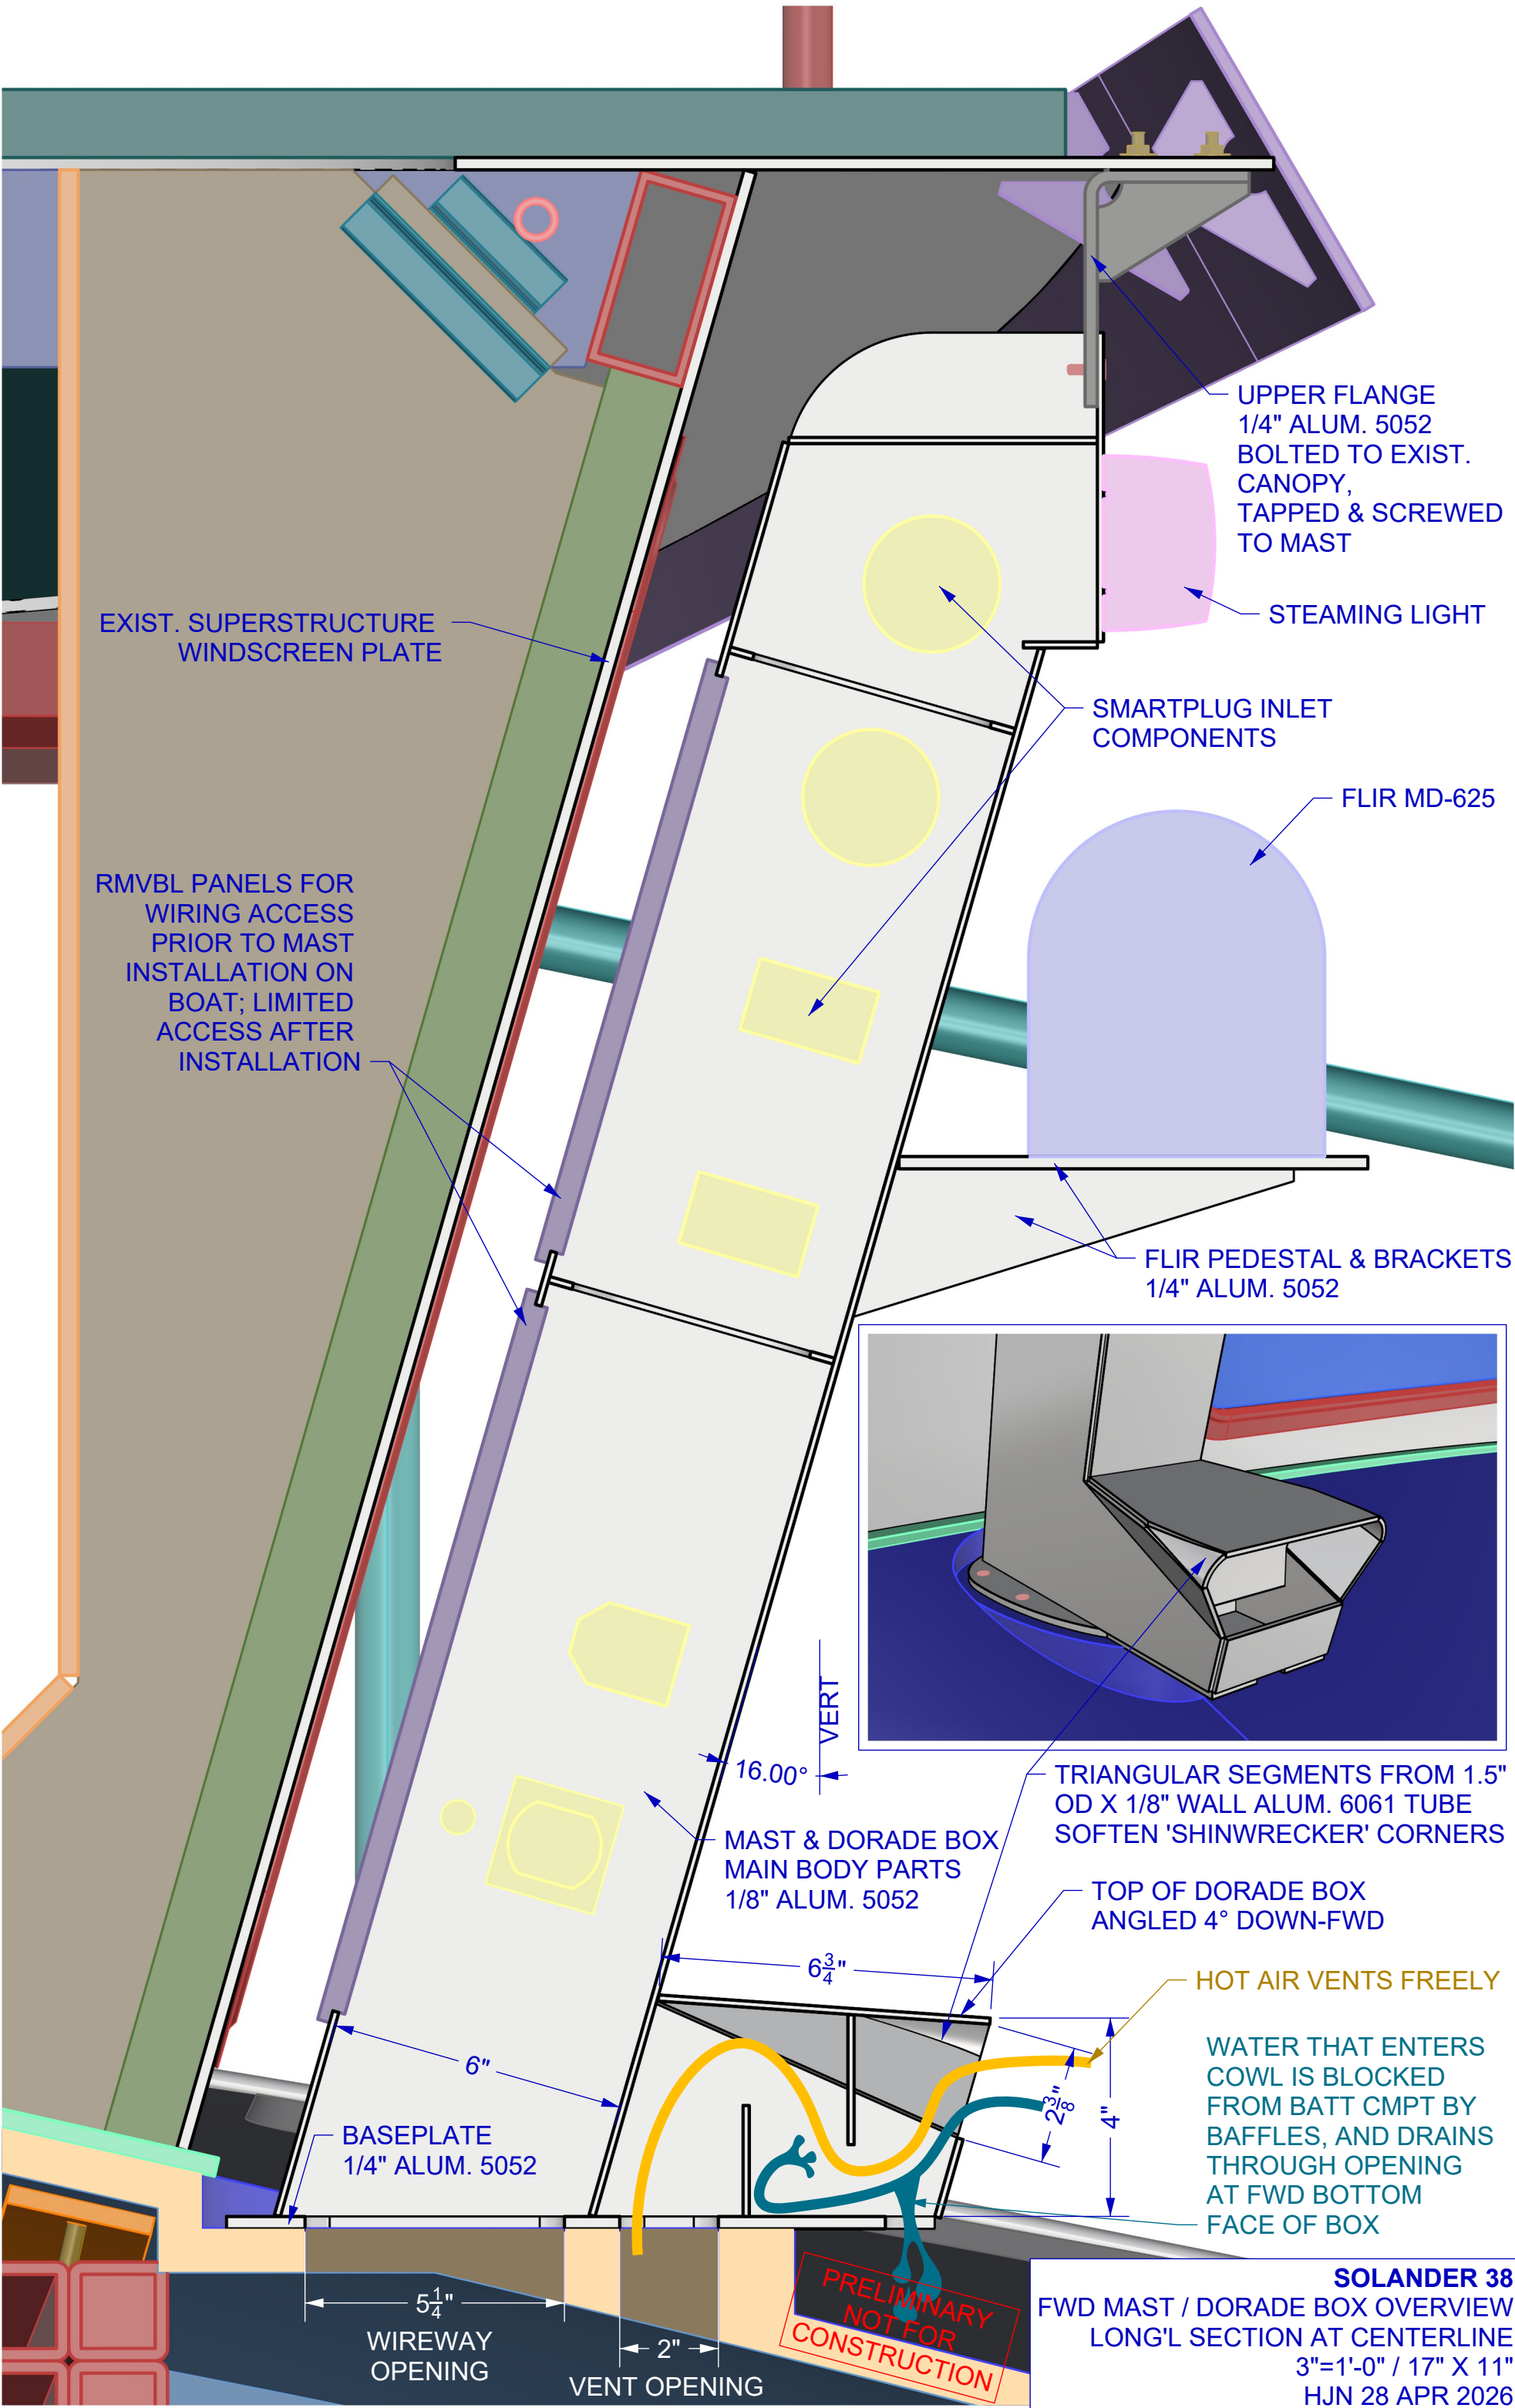

SOLANDER 38
FWD MAST / DORADE BOX OVERVIEW
LONG'L SECTION AT CENTERLINE
3"=1'-0" / 17" X 11"
HJN 28 APR 2026